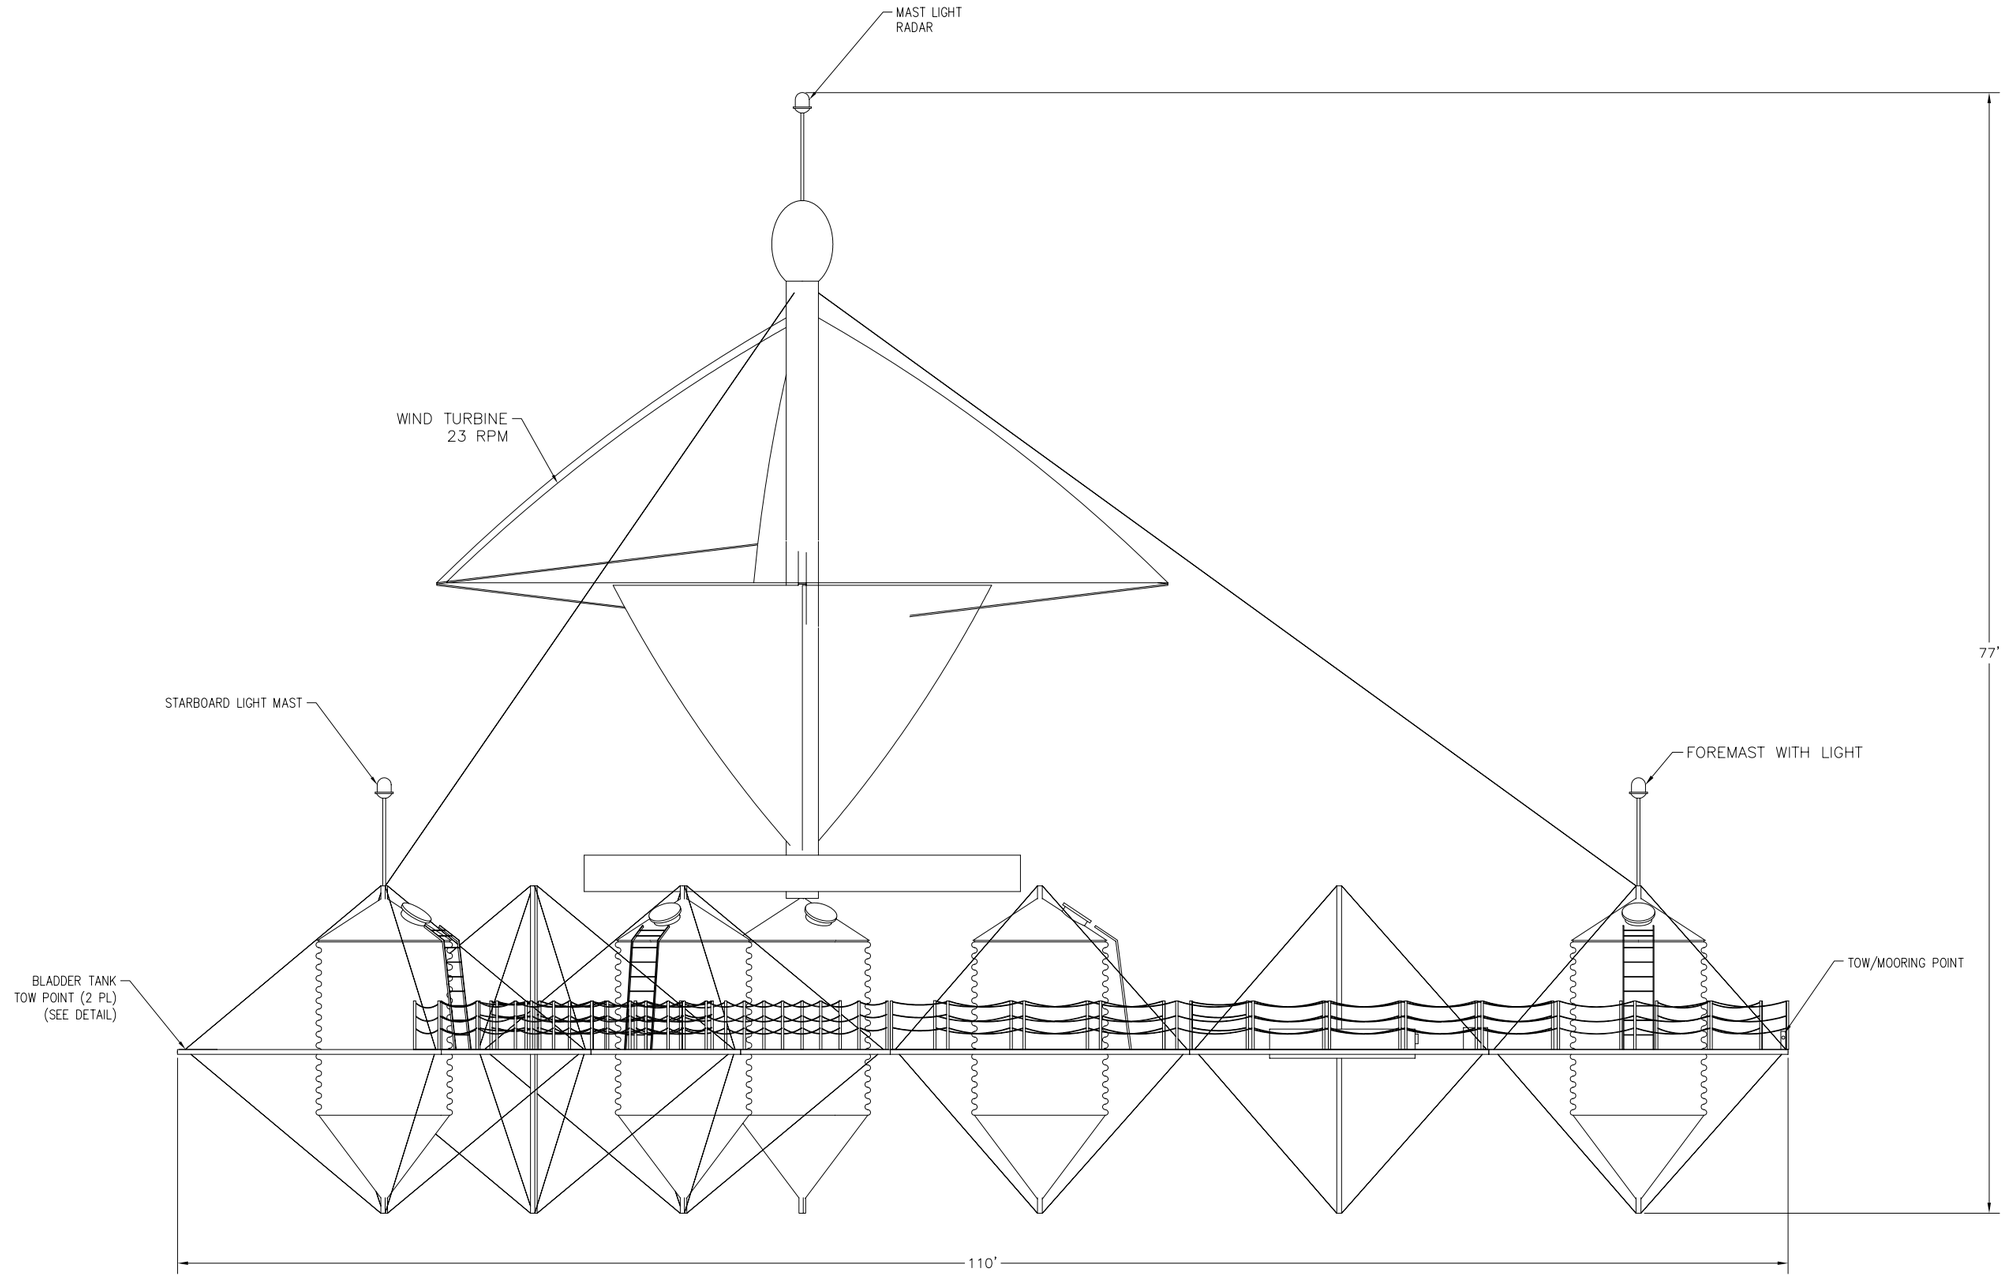


ELEVATION 20-A

FLOATATION FRAME WITH OUT STORAGE BLADDER

SCALE: 1/4 = 1FT-0IN

DRAWING TITLE: GENERAL ARRANGEMENT OCEAN GYPSY		
SIZE F	DRAWING NO. 1157-001-01	REV –
SCALE: AS SHOWN		SHEET 3 OF 3