
GENERAL NOTES

1. DUMP VALVE TO OPEN UPON LOSS OF ELECTRIC POWER.
2. PURGE PUMP WILL RUN WHEN PRESSURE DROPS TO 2 PSIG.

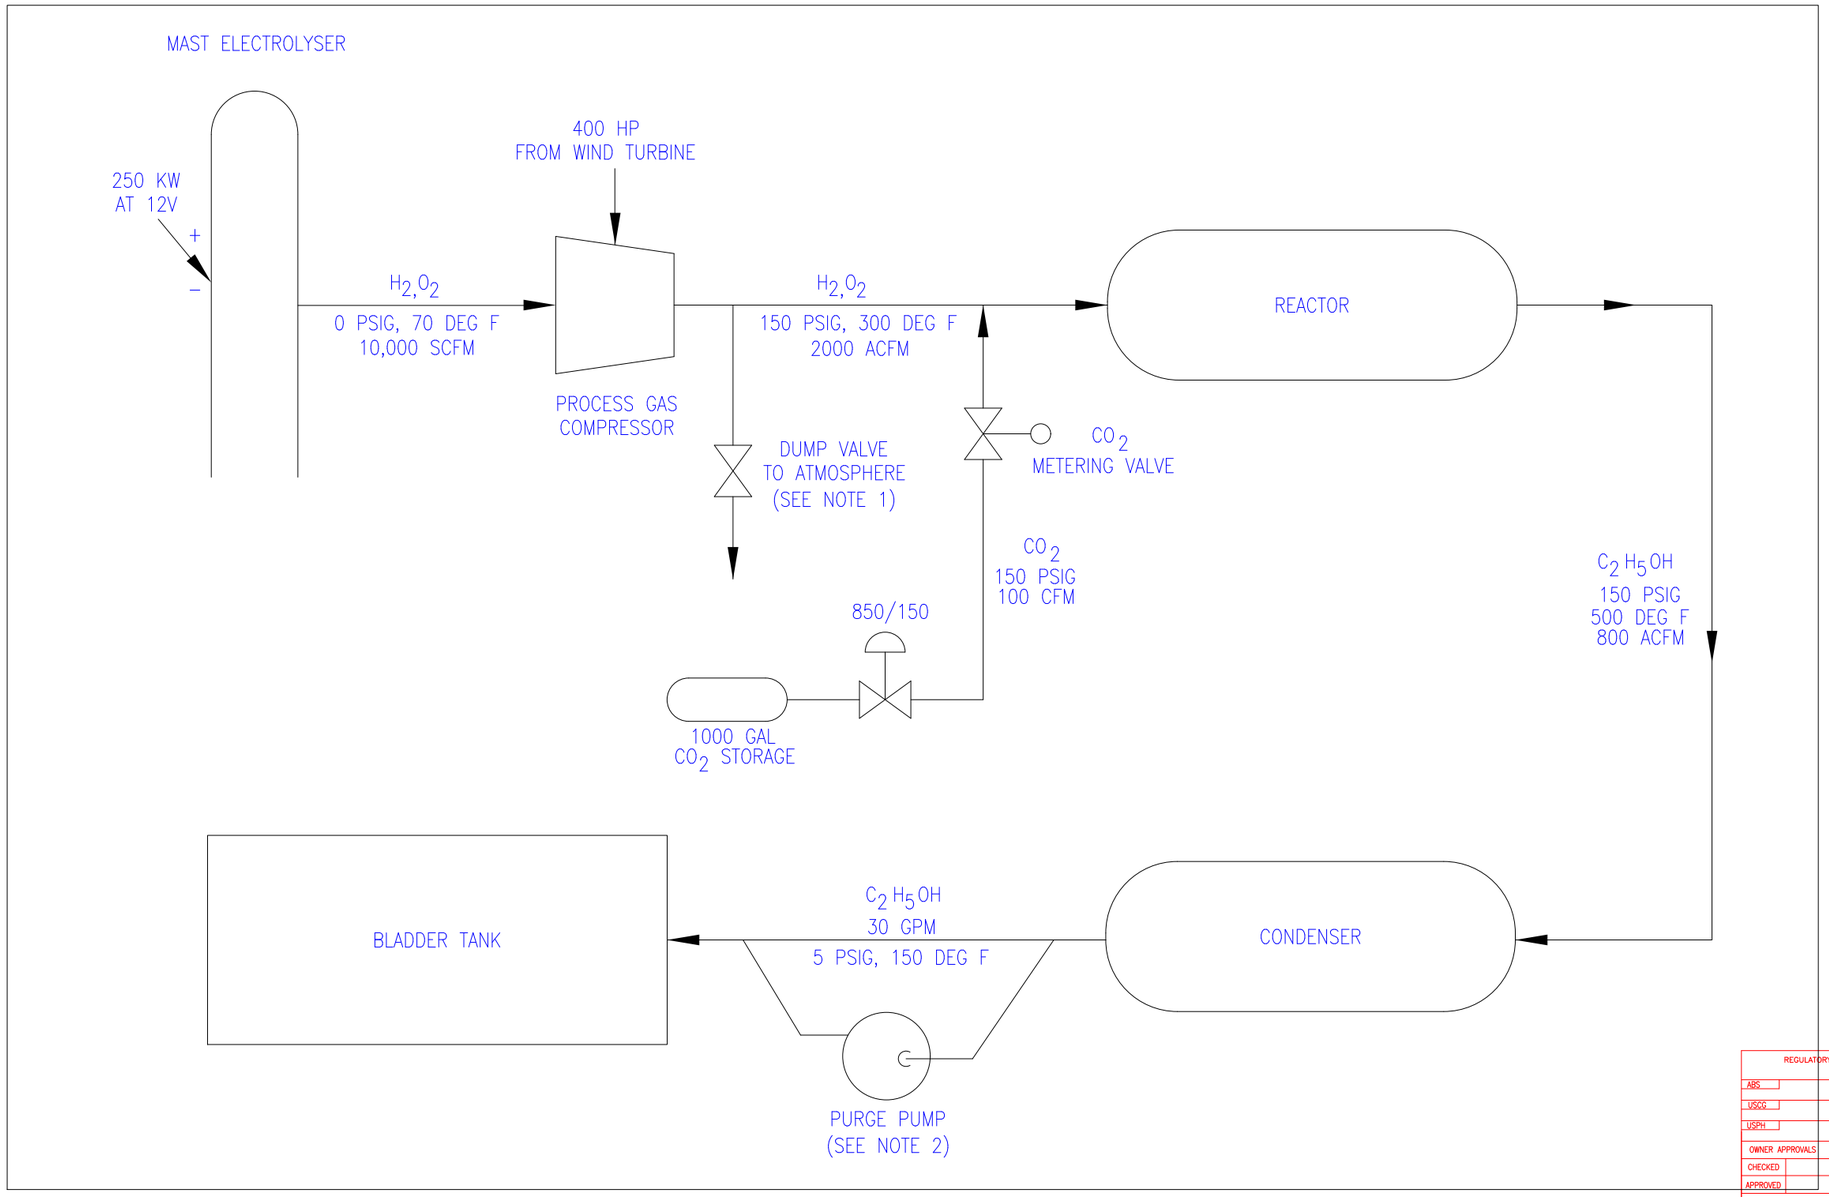

PROPRIETARY

DO NOT DISTRIBUTE WITHOUT PERMISSION.

REGULATORY BODY		NDI ENGINEERING COMPANY RESEARCH AND CONSULTING ENGINEERS 100 GROVE ROAD THOROFARE, NJ 08086	
ABS		SHIP: OGP-X "Herman Behrens"	
USCG		LOCATION:	
USPH		DRAWING TITLE: ETHANOL PROCESS FLOW DIAGRAM OCEAN GYPSY	
OWNER APPROVALS		SIZE: F	DRAWING NO.: 1157-001-02
CHECKED	DATE	REV: –	
APPROVED		SCALE: NONE	SHEET 1 OF 1
REVISED			
• DO NOT SCALE DRAWING			
APPRVD			
CHKD			
DRAWN	SCOTT 10/13/04		